
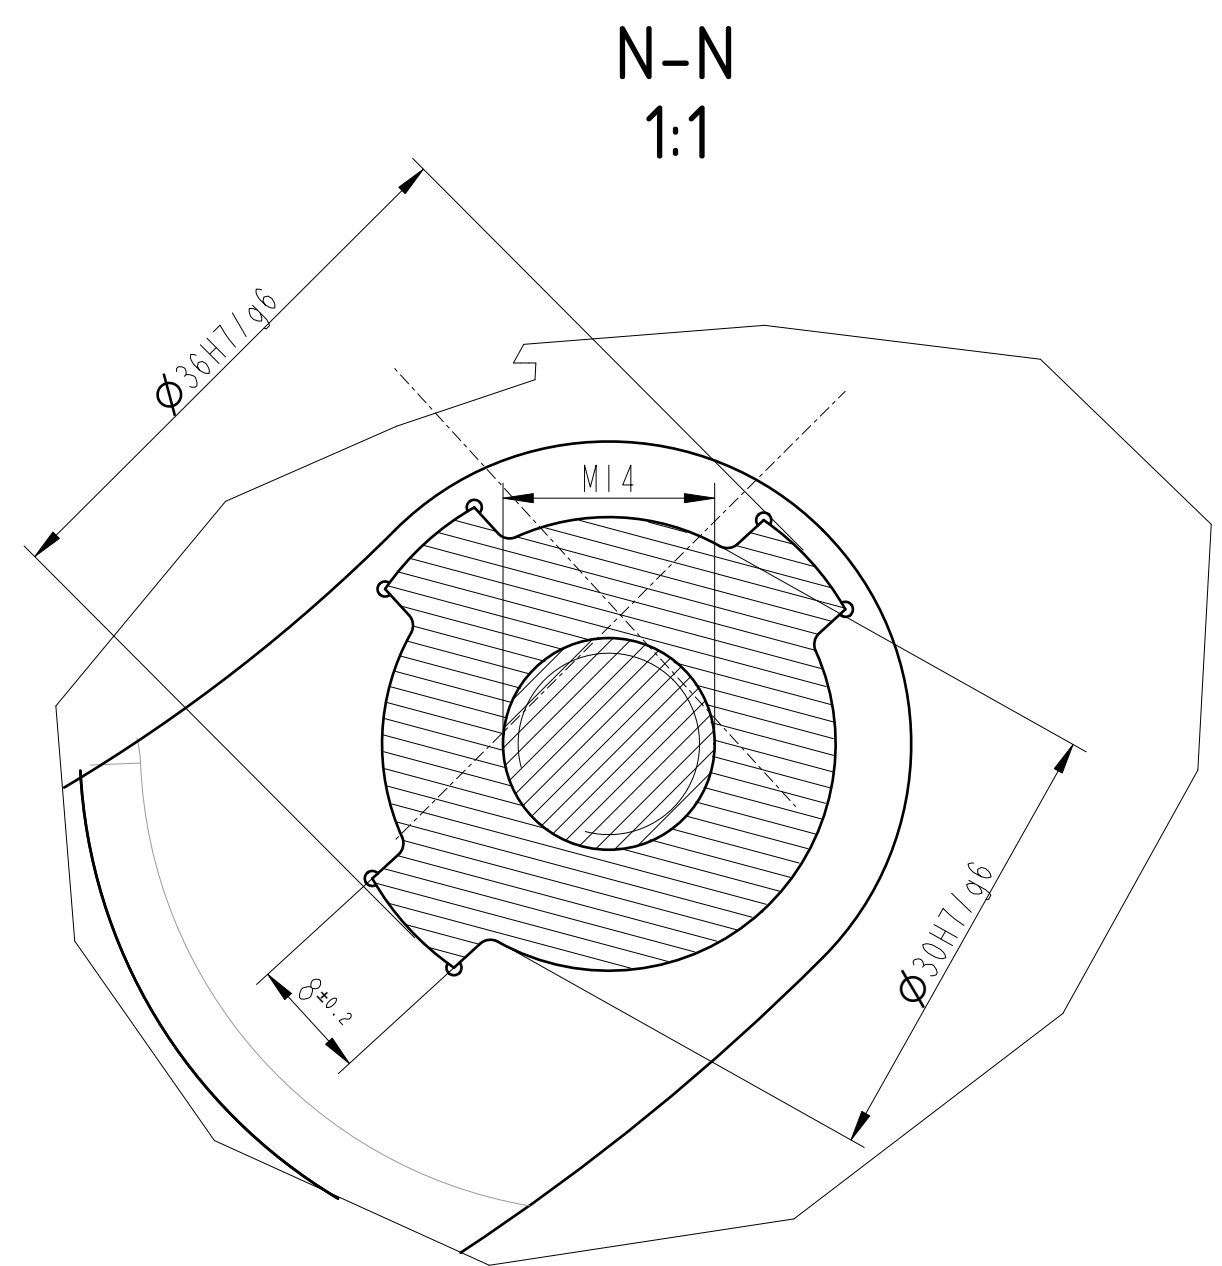
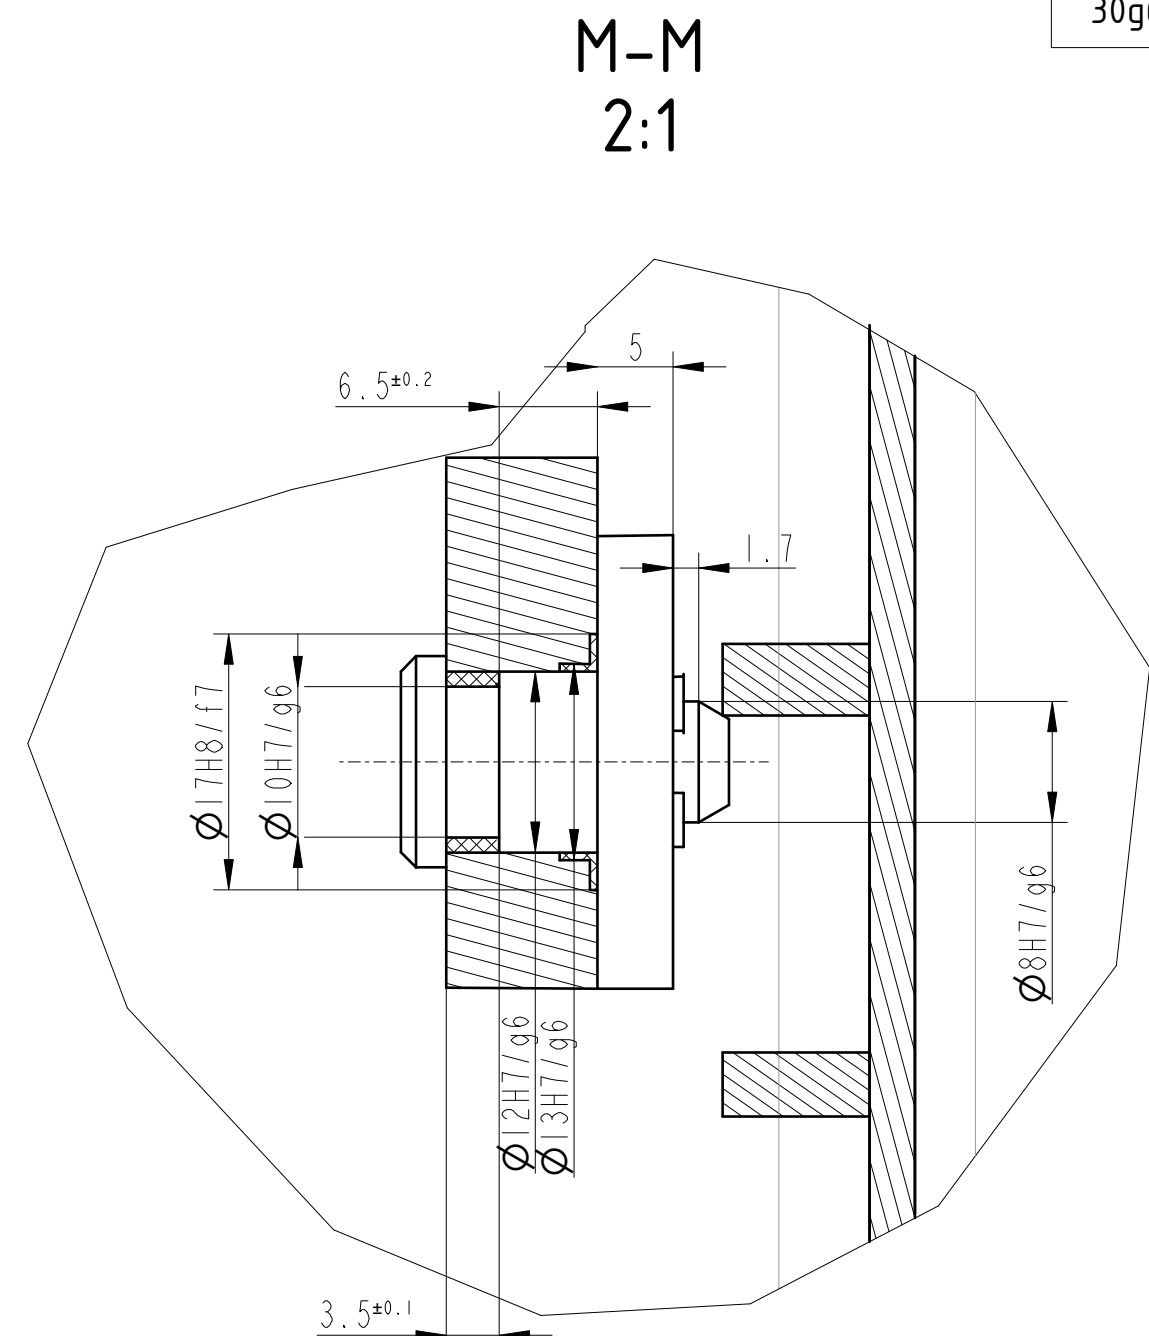
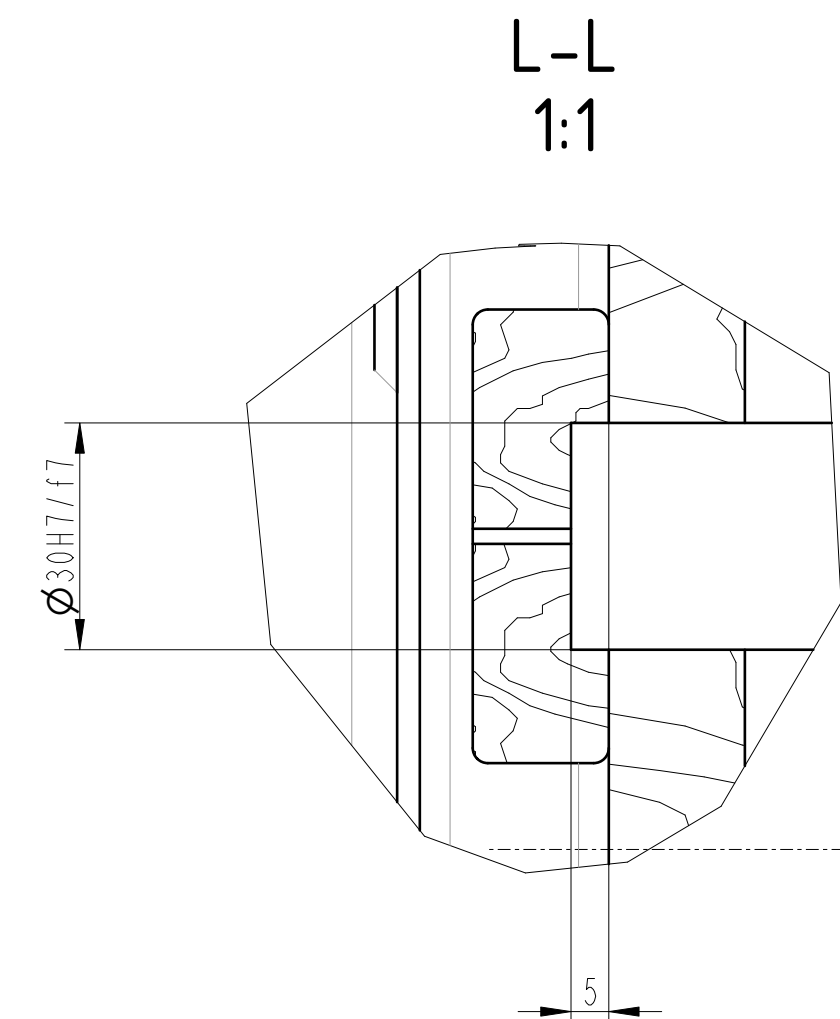
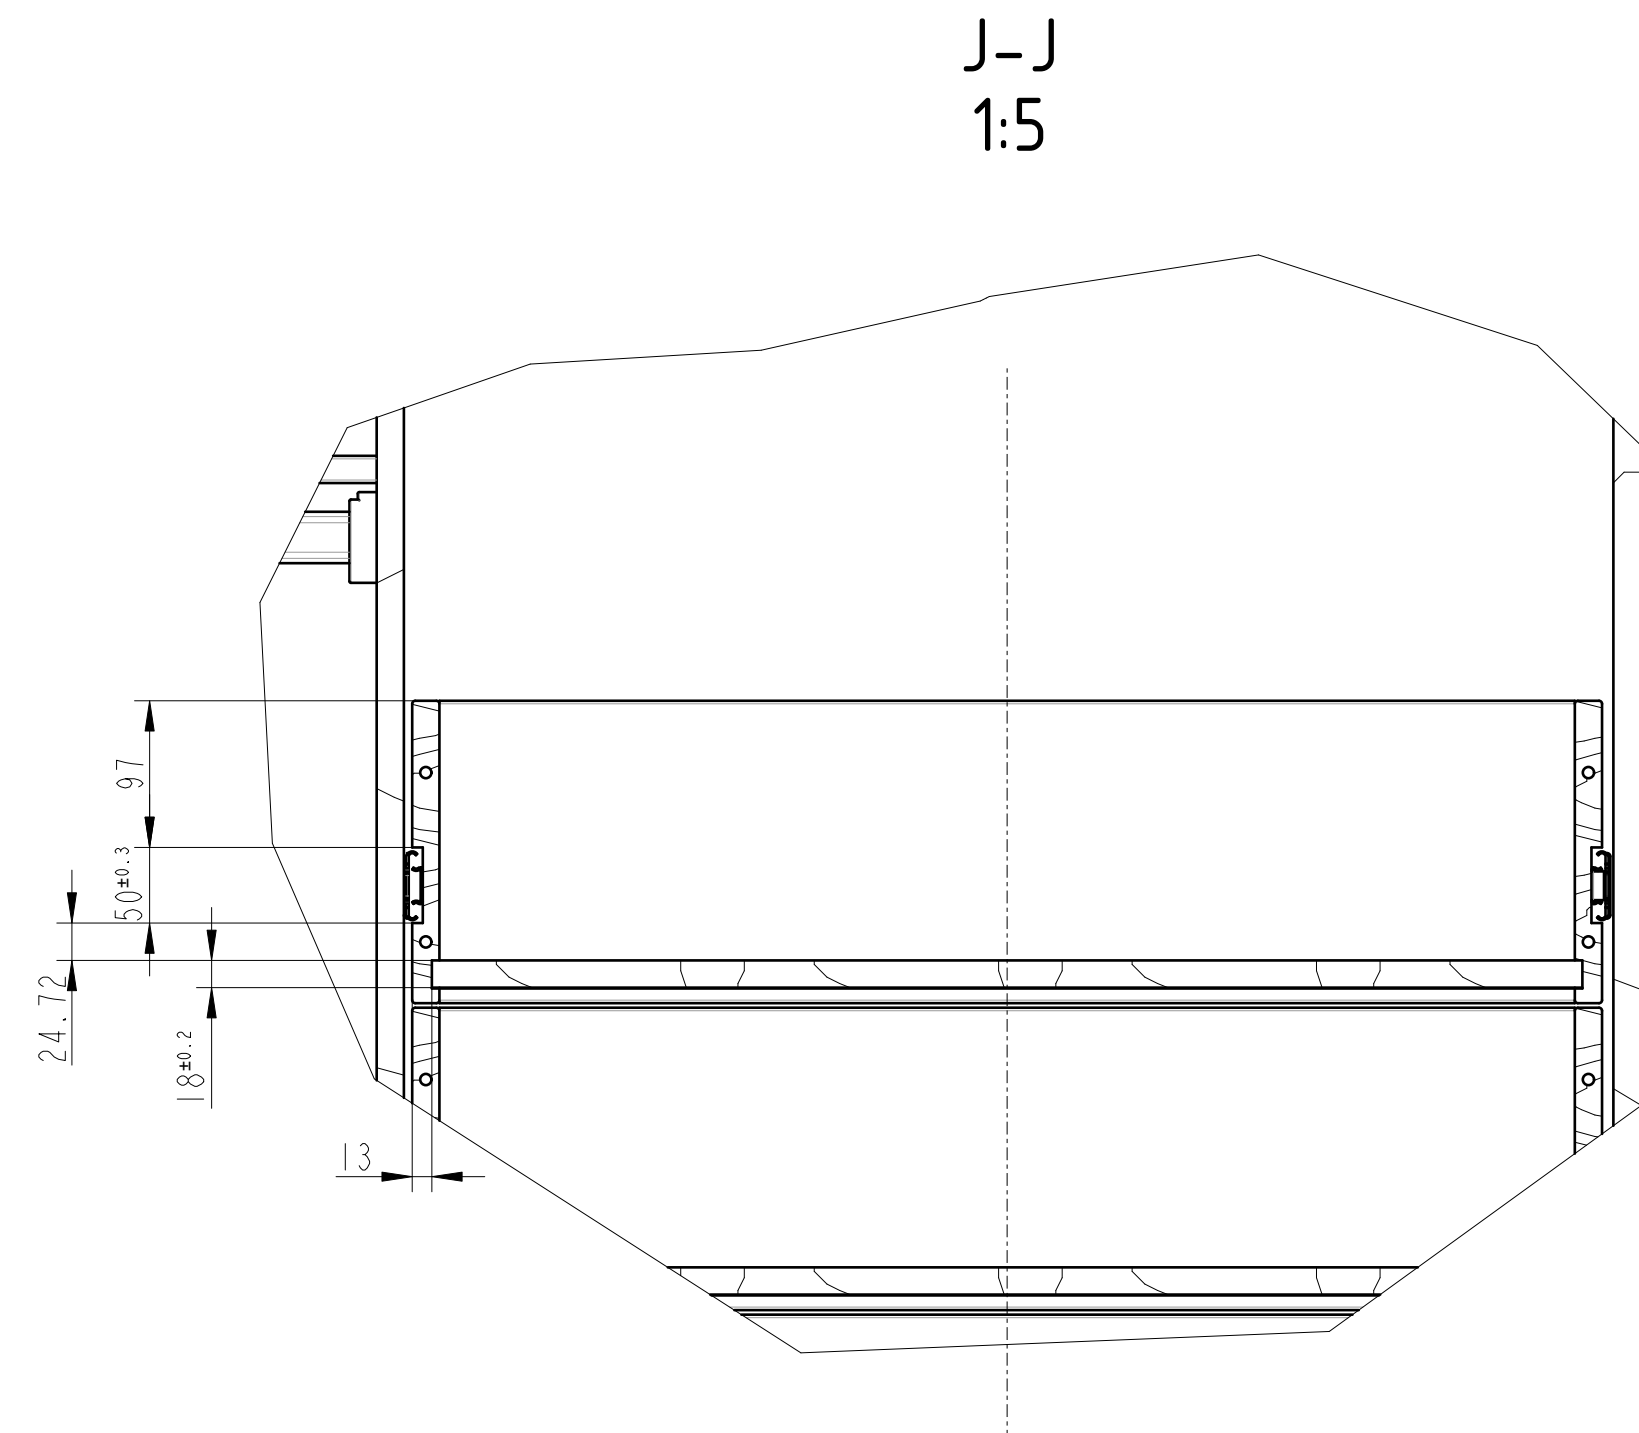
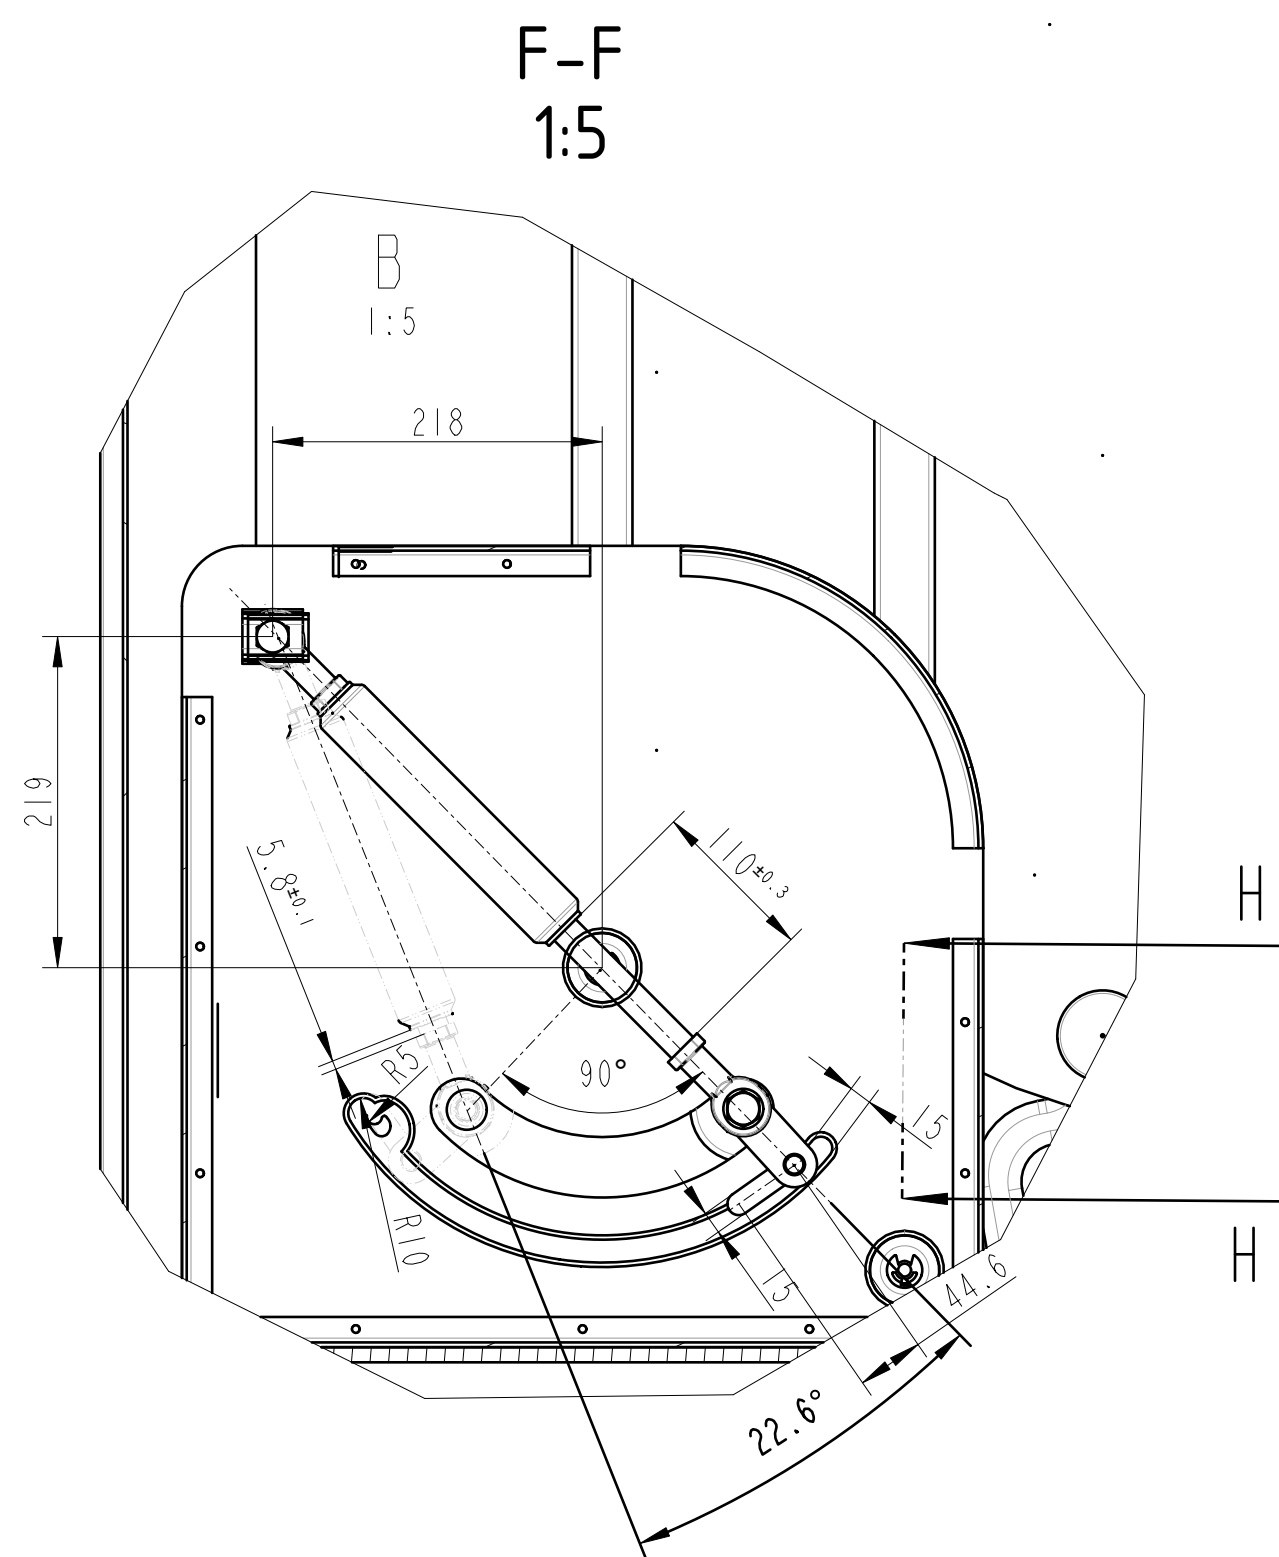
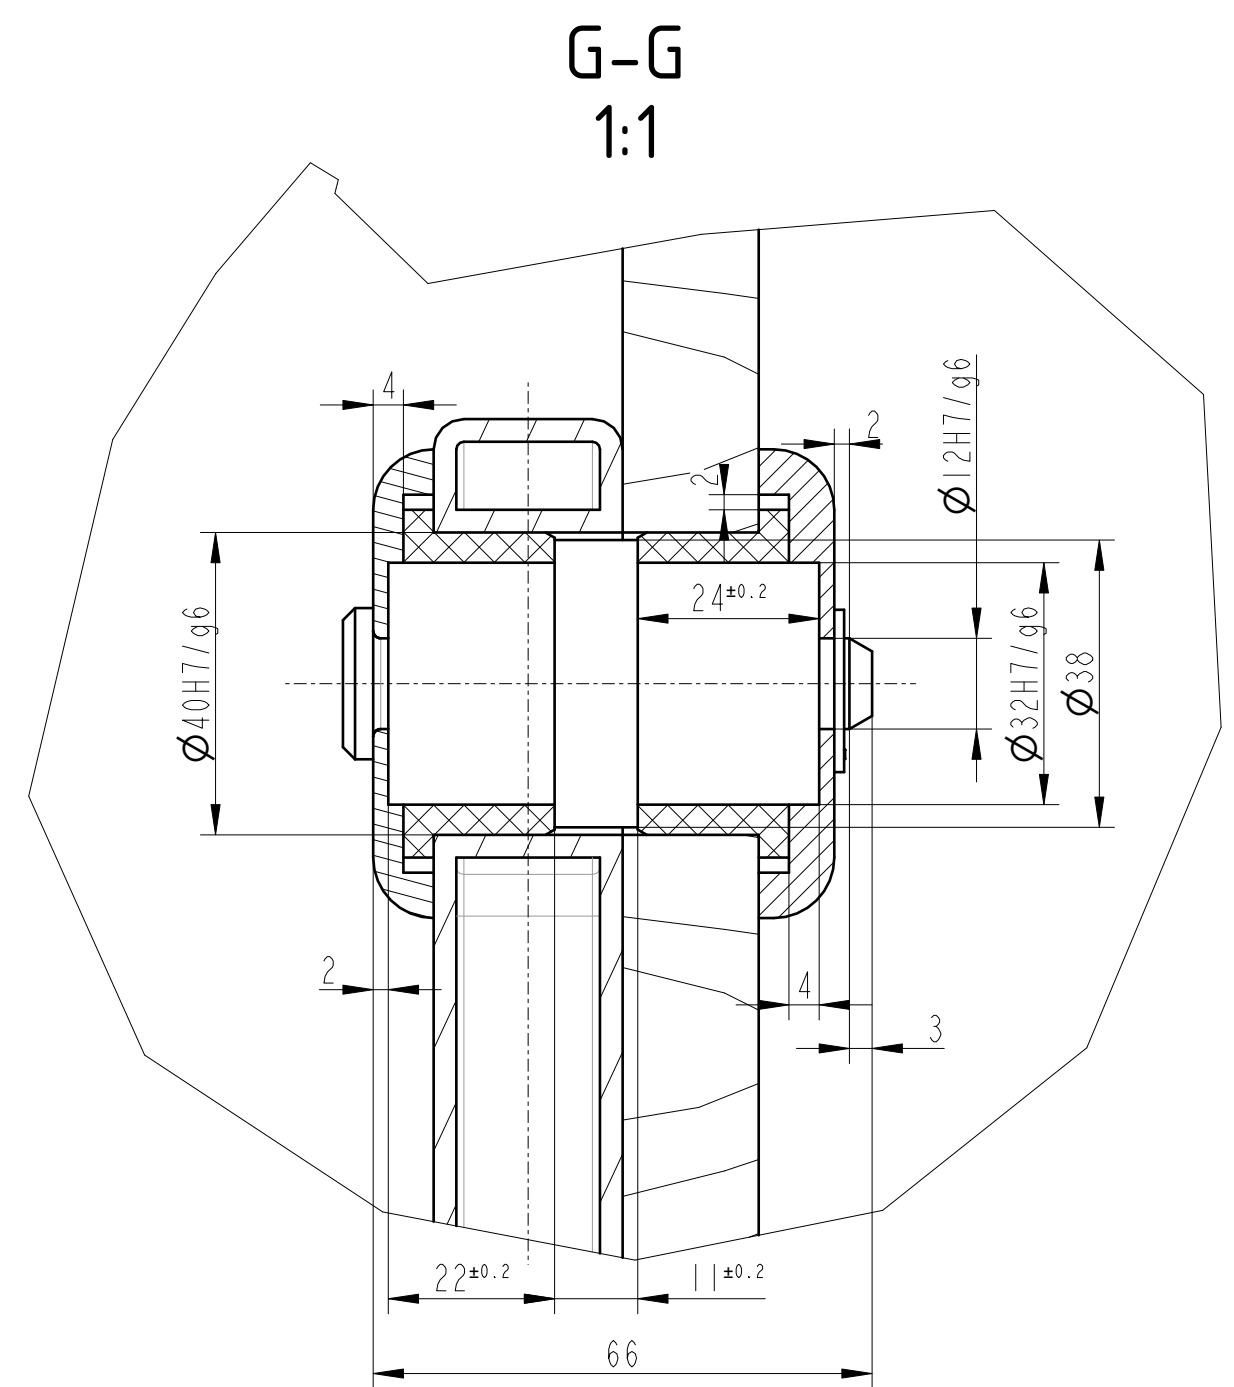
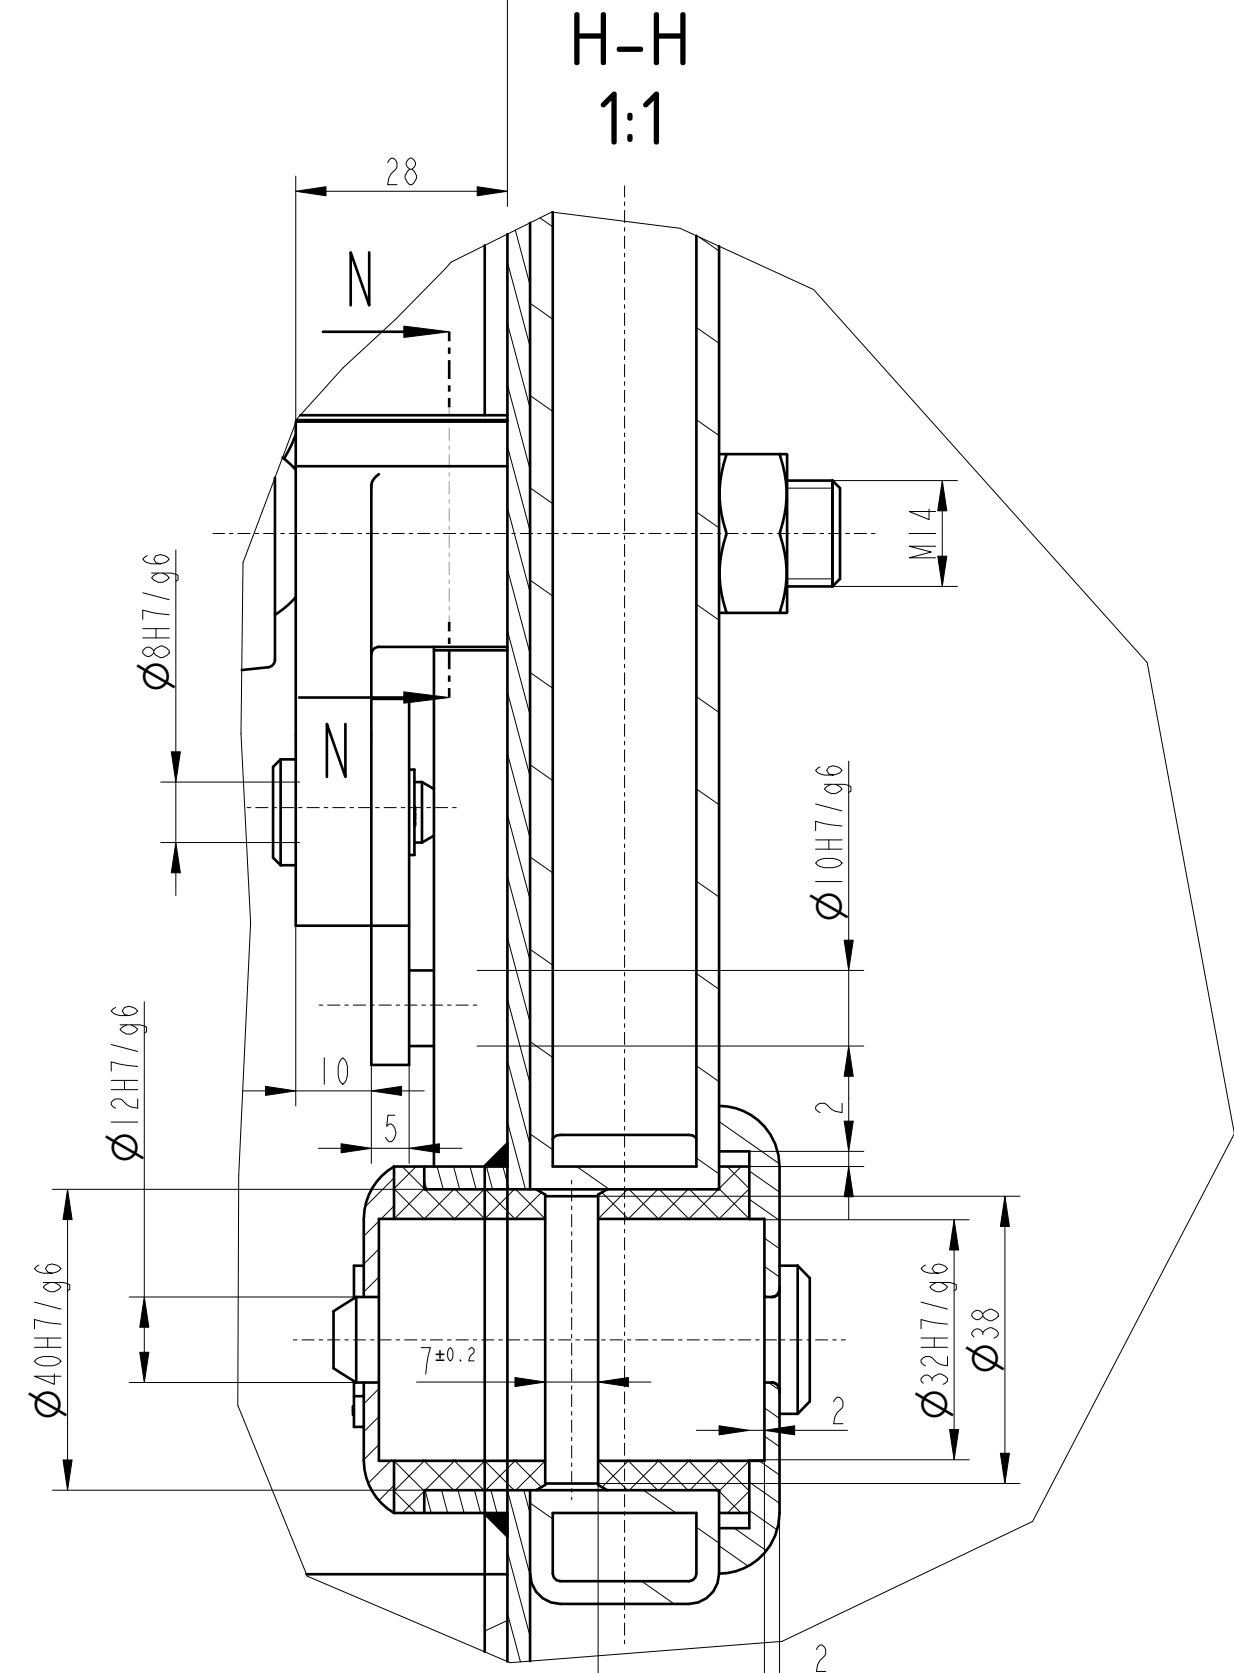
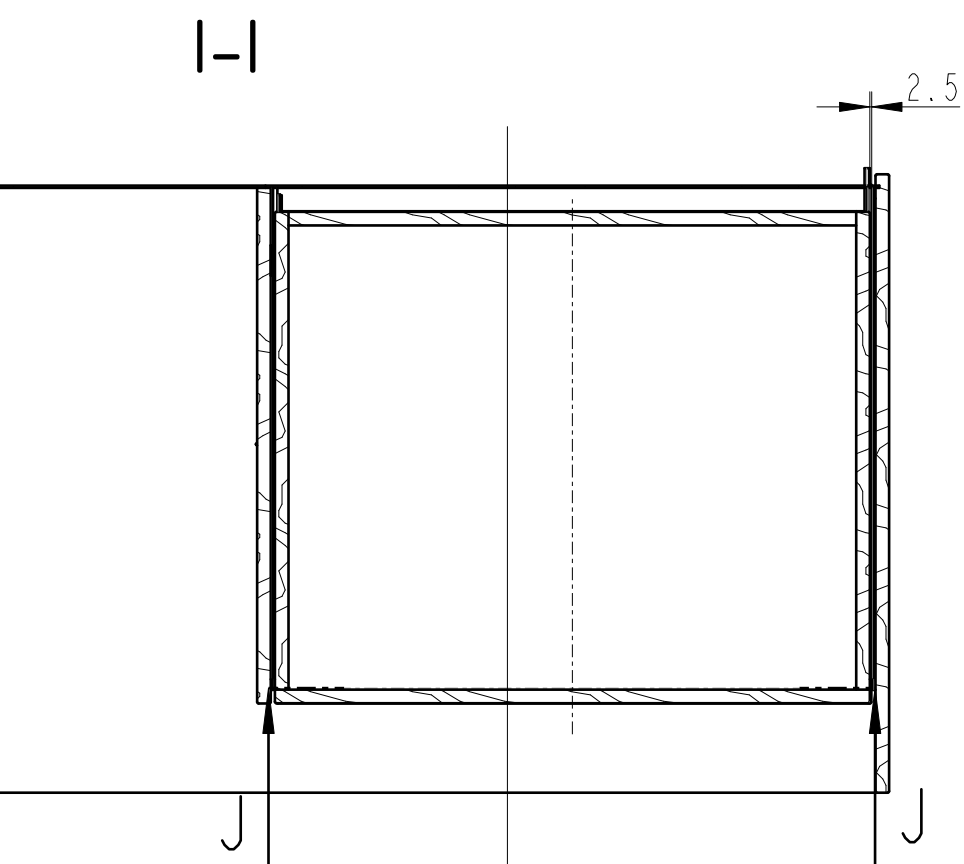
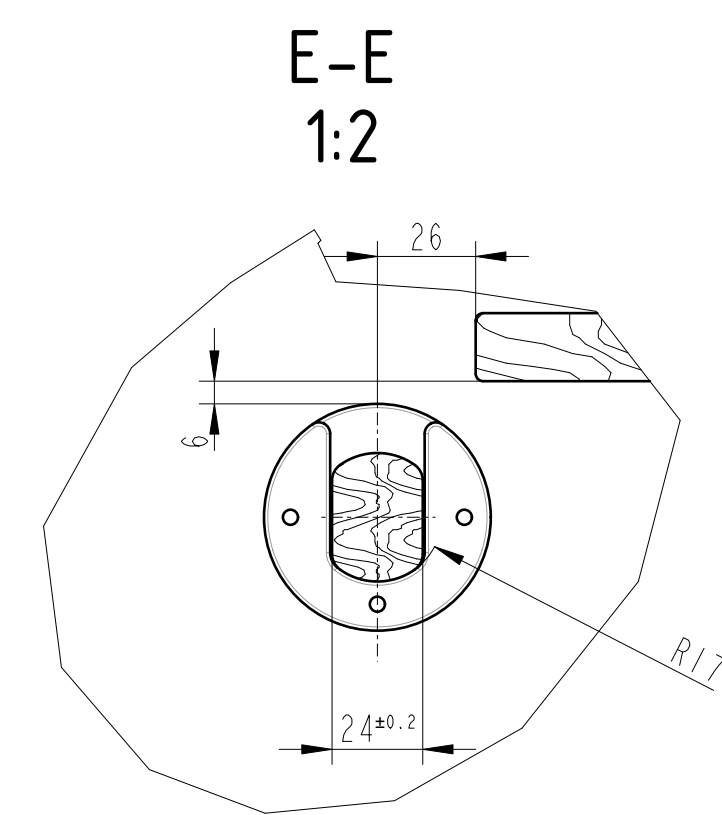
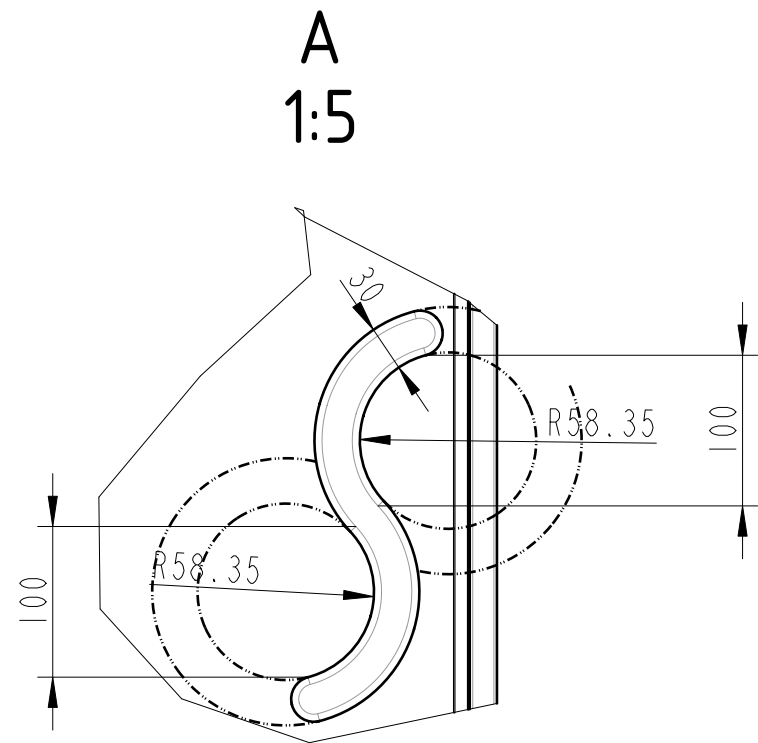
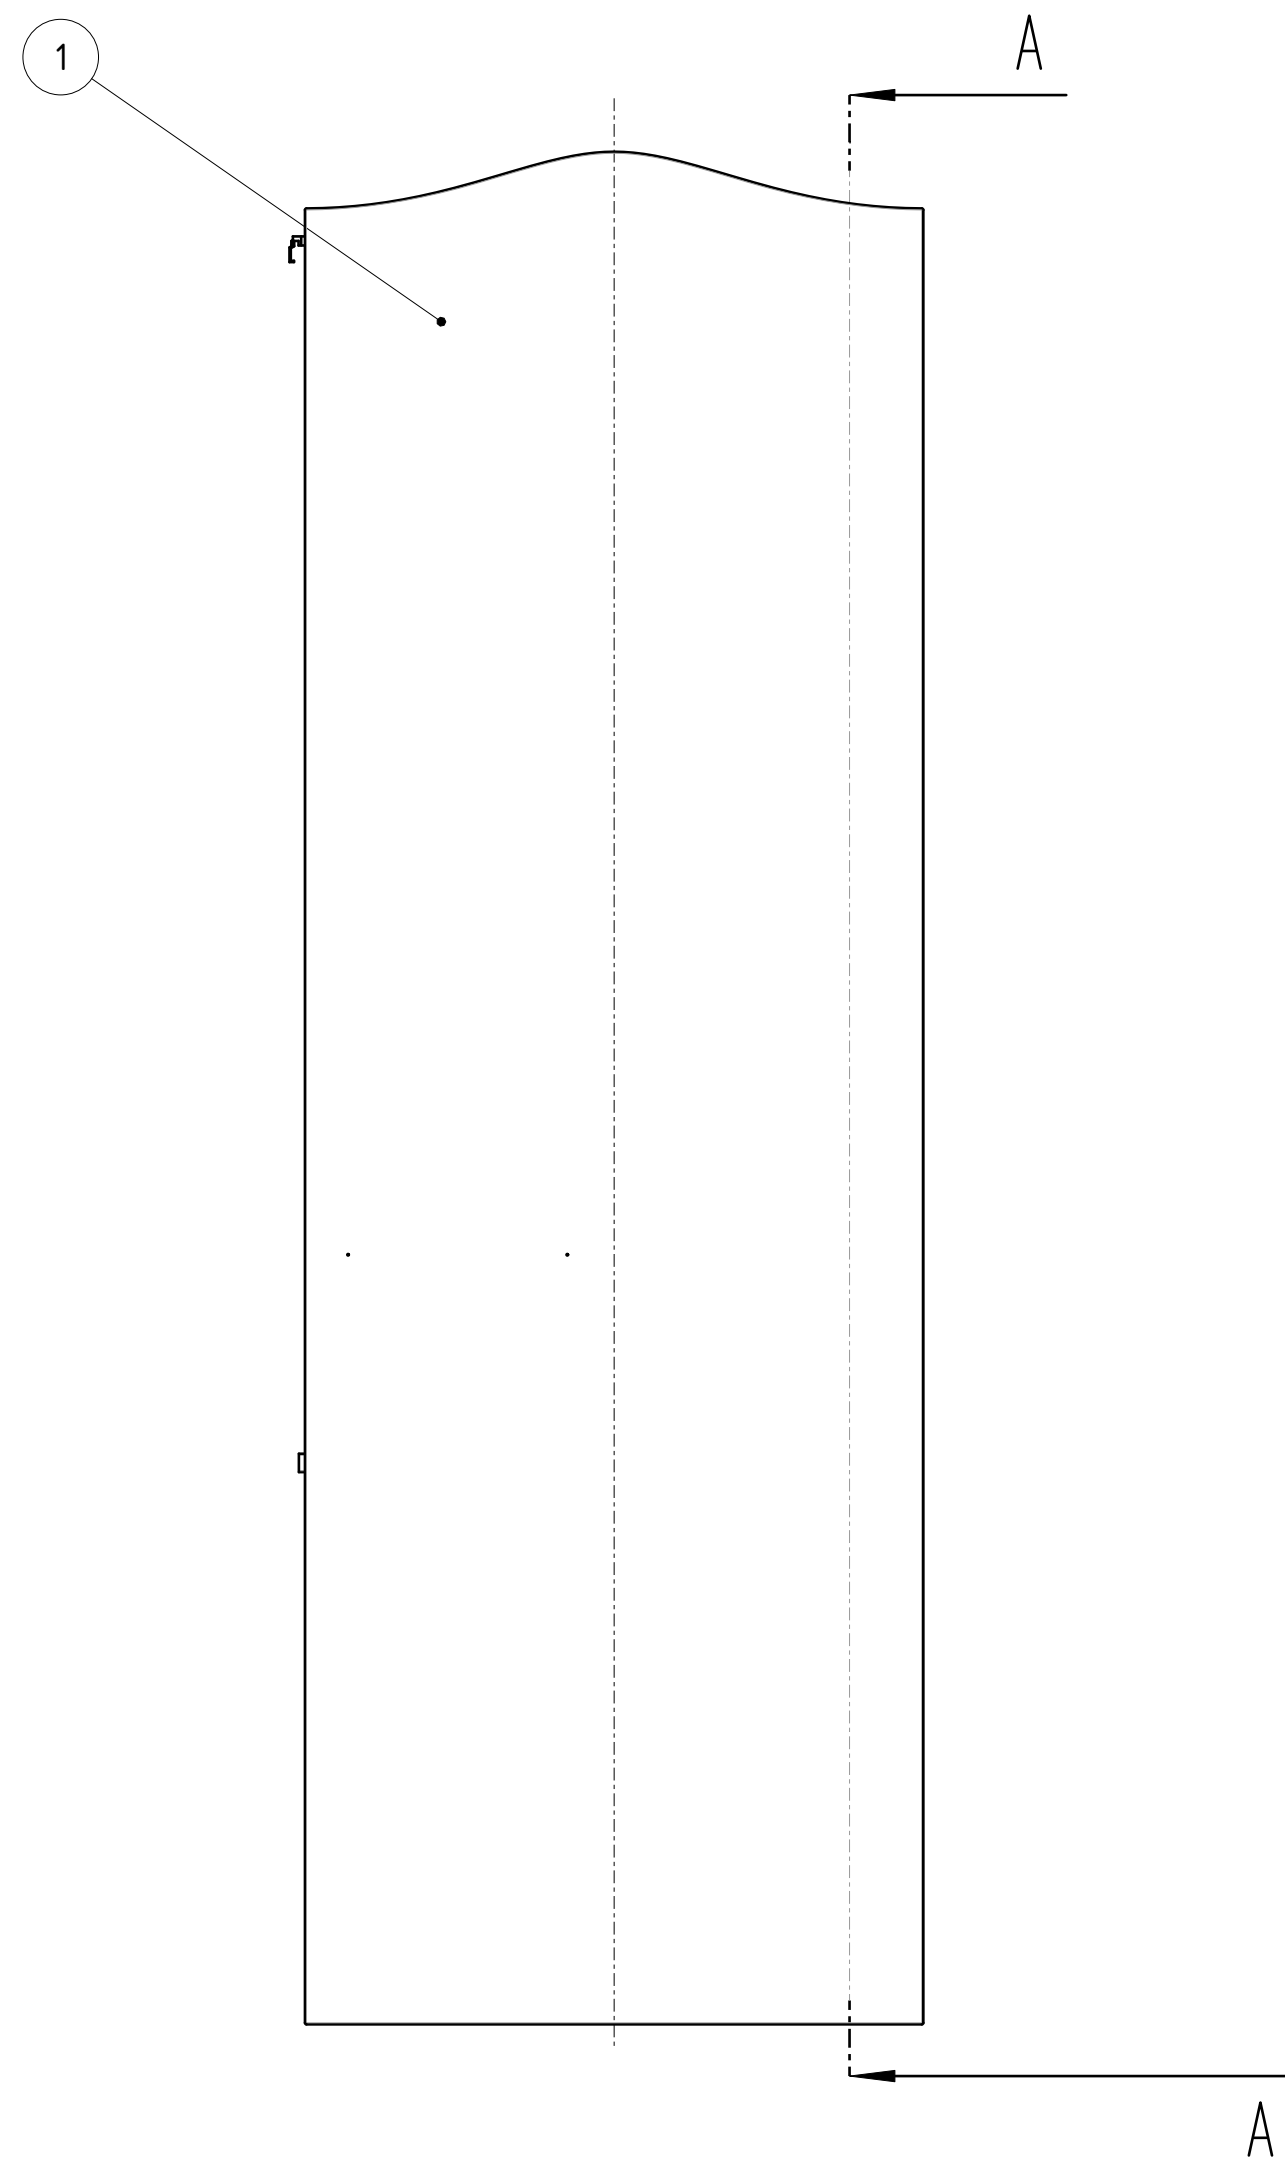
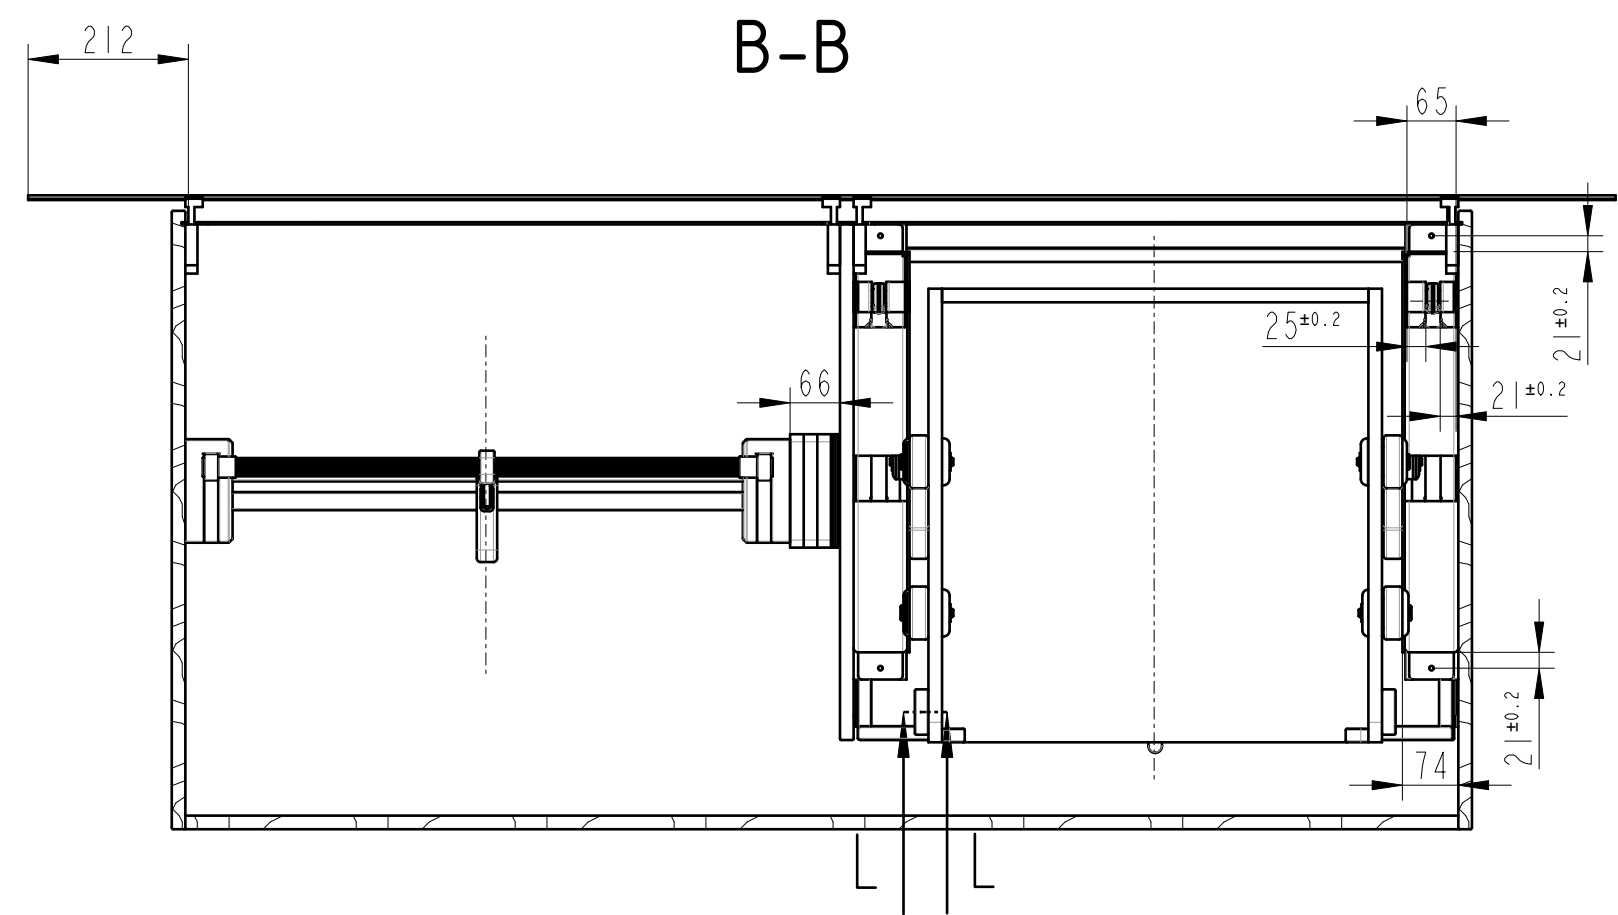
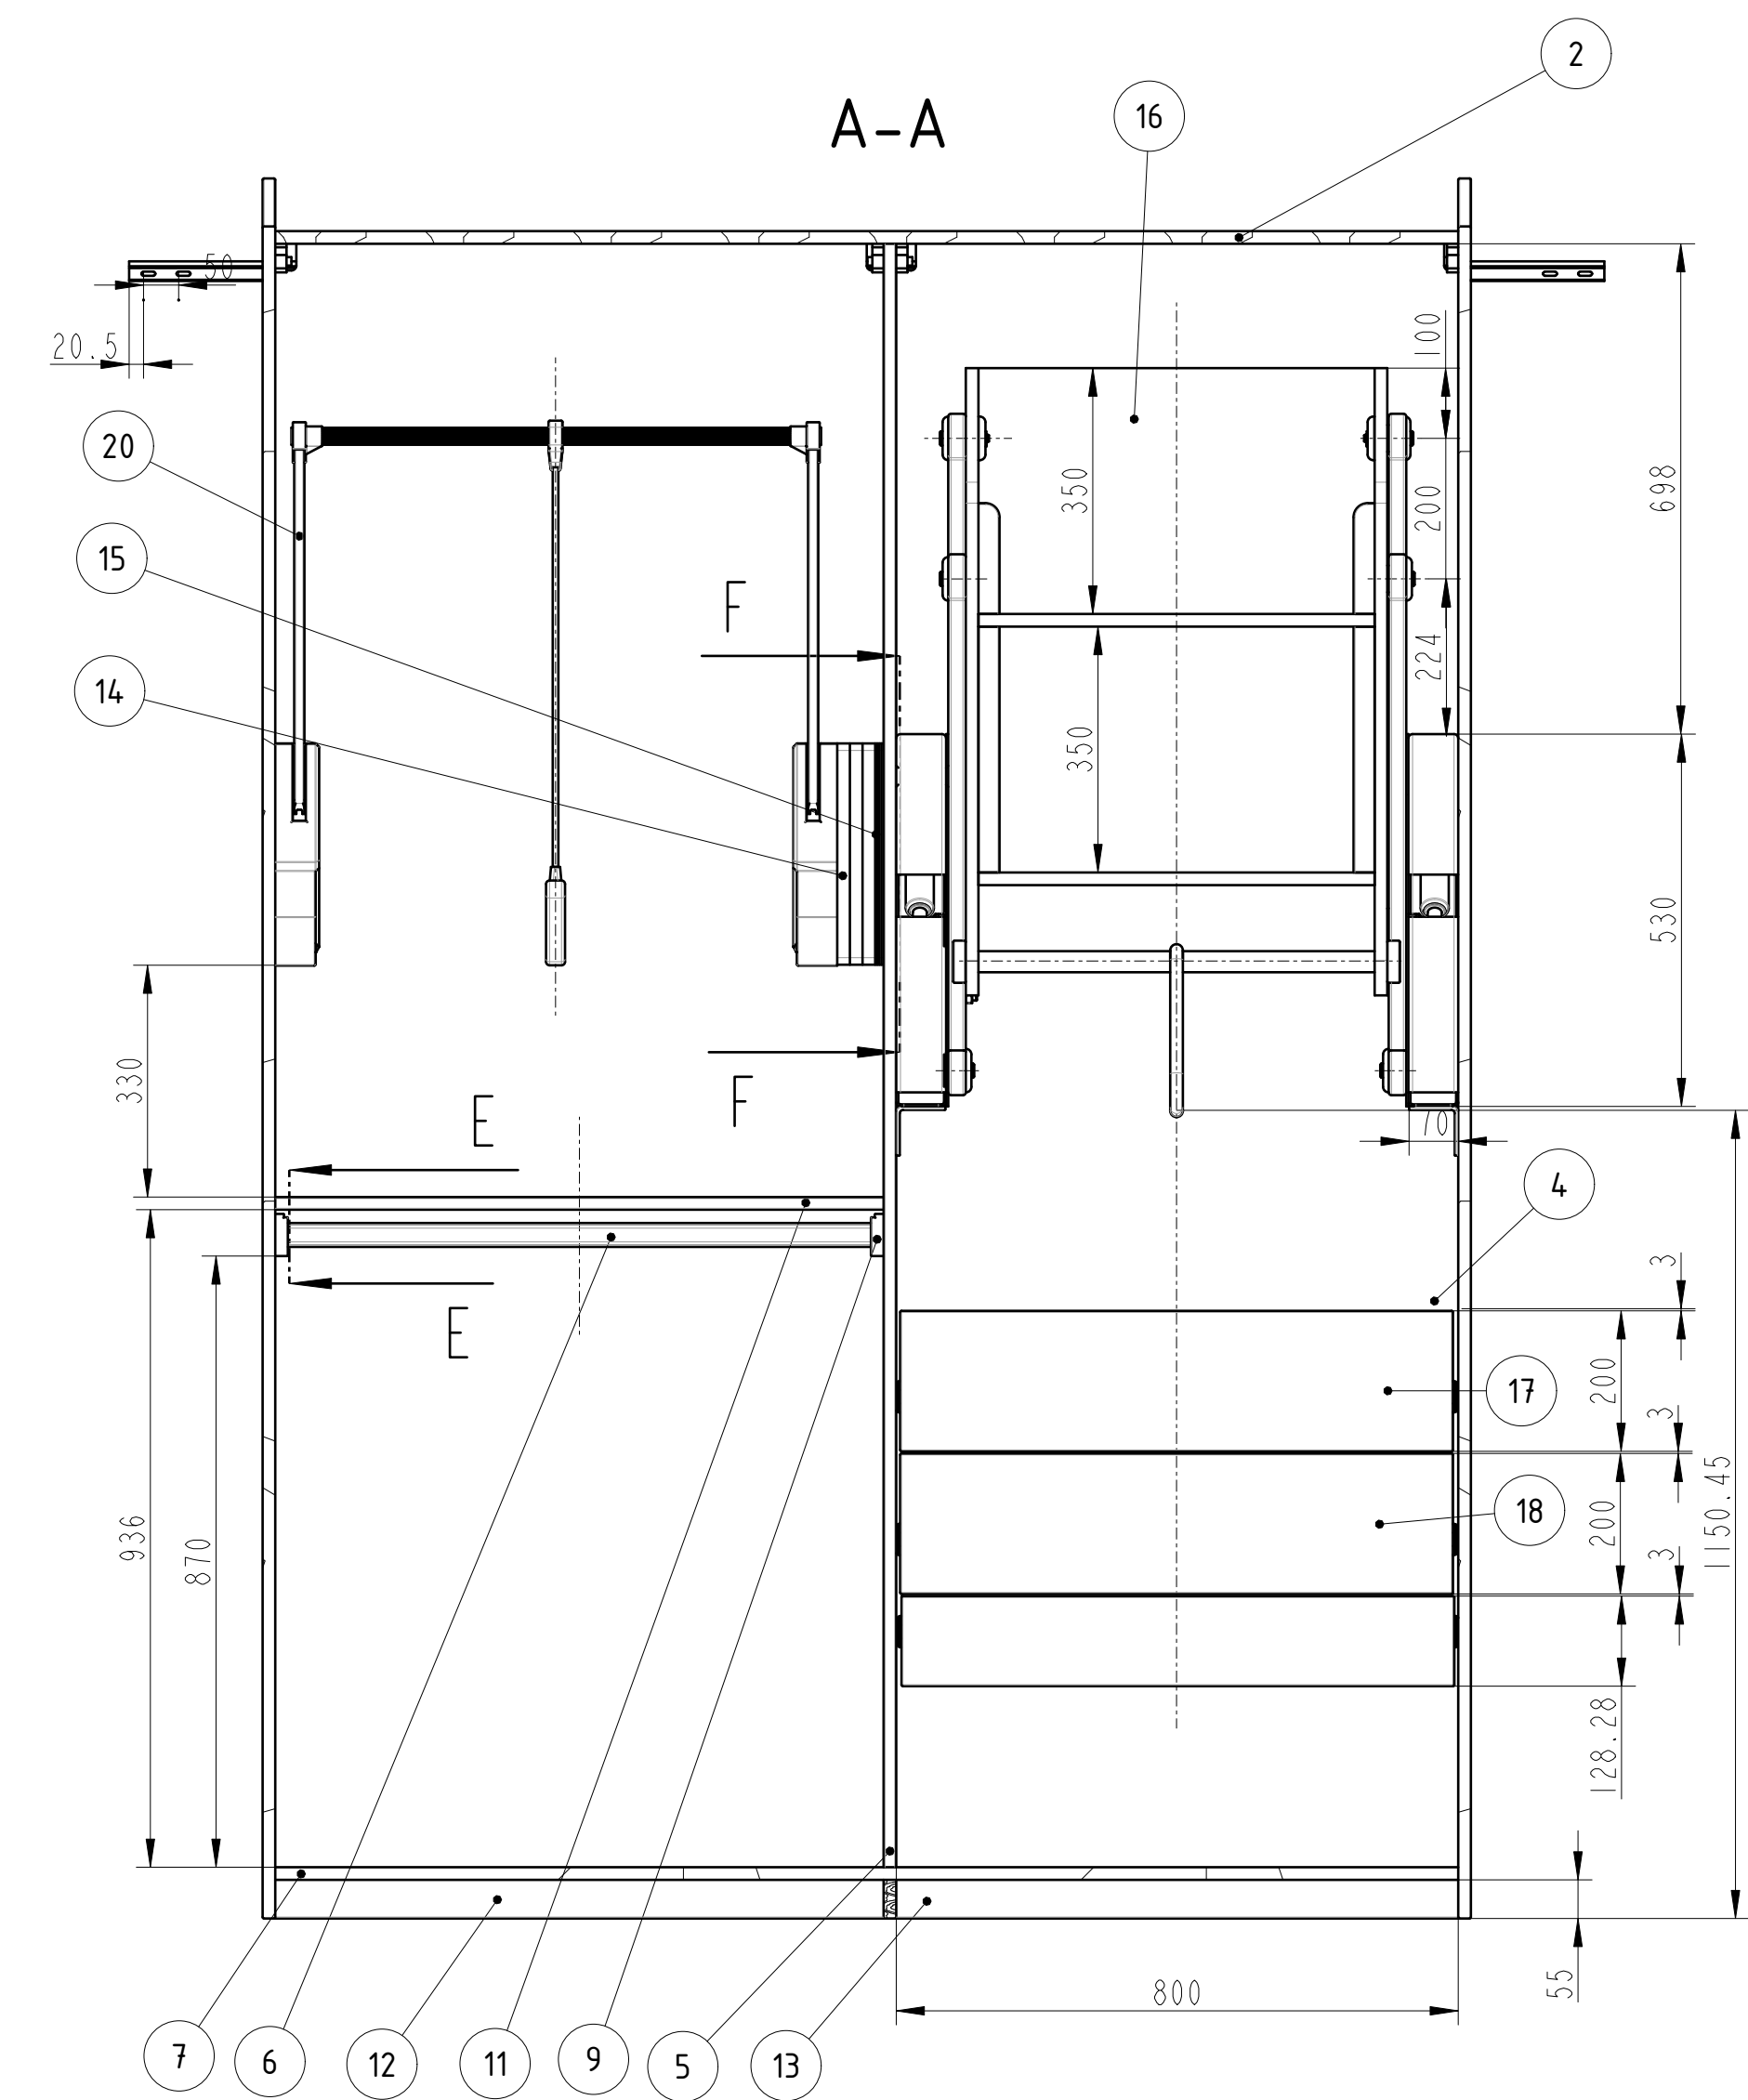
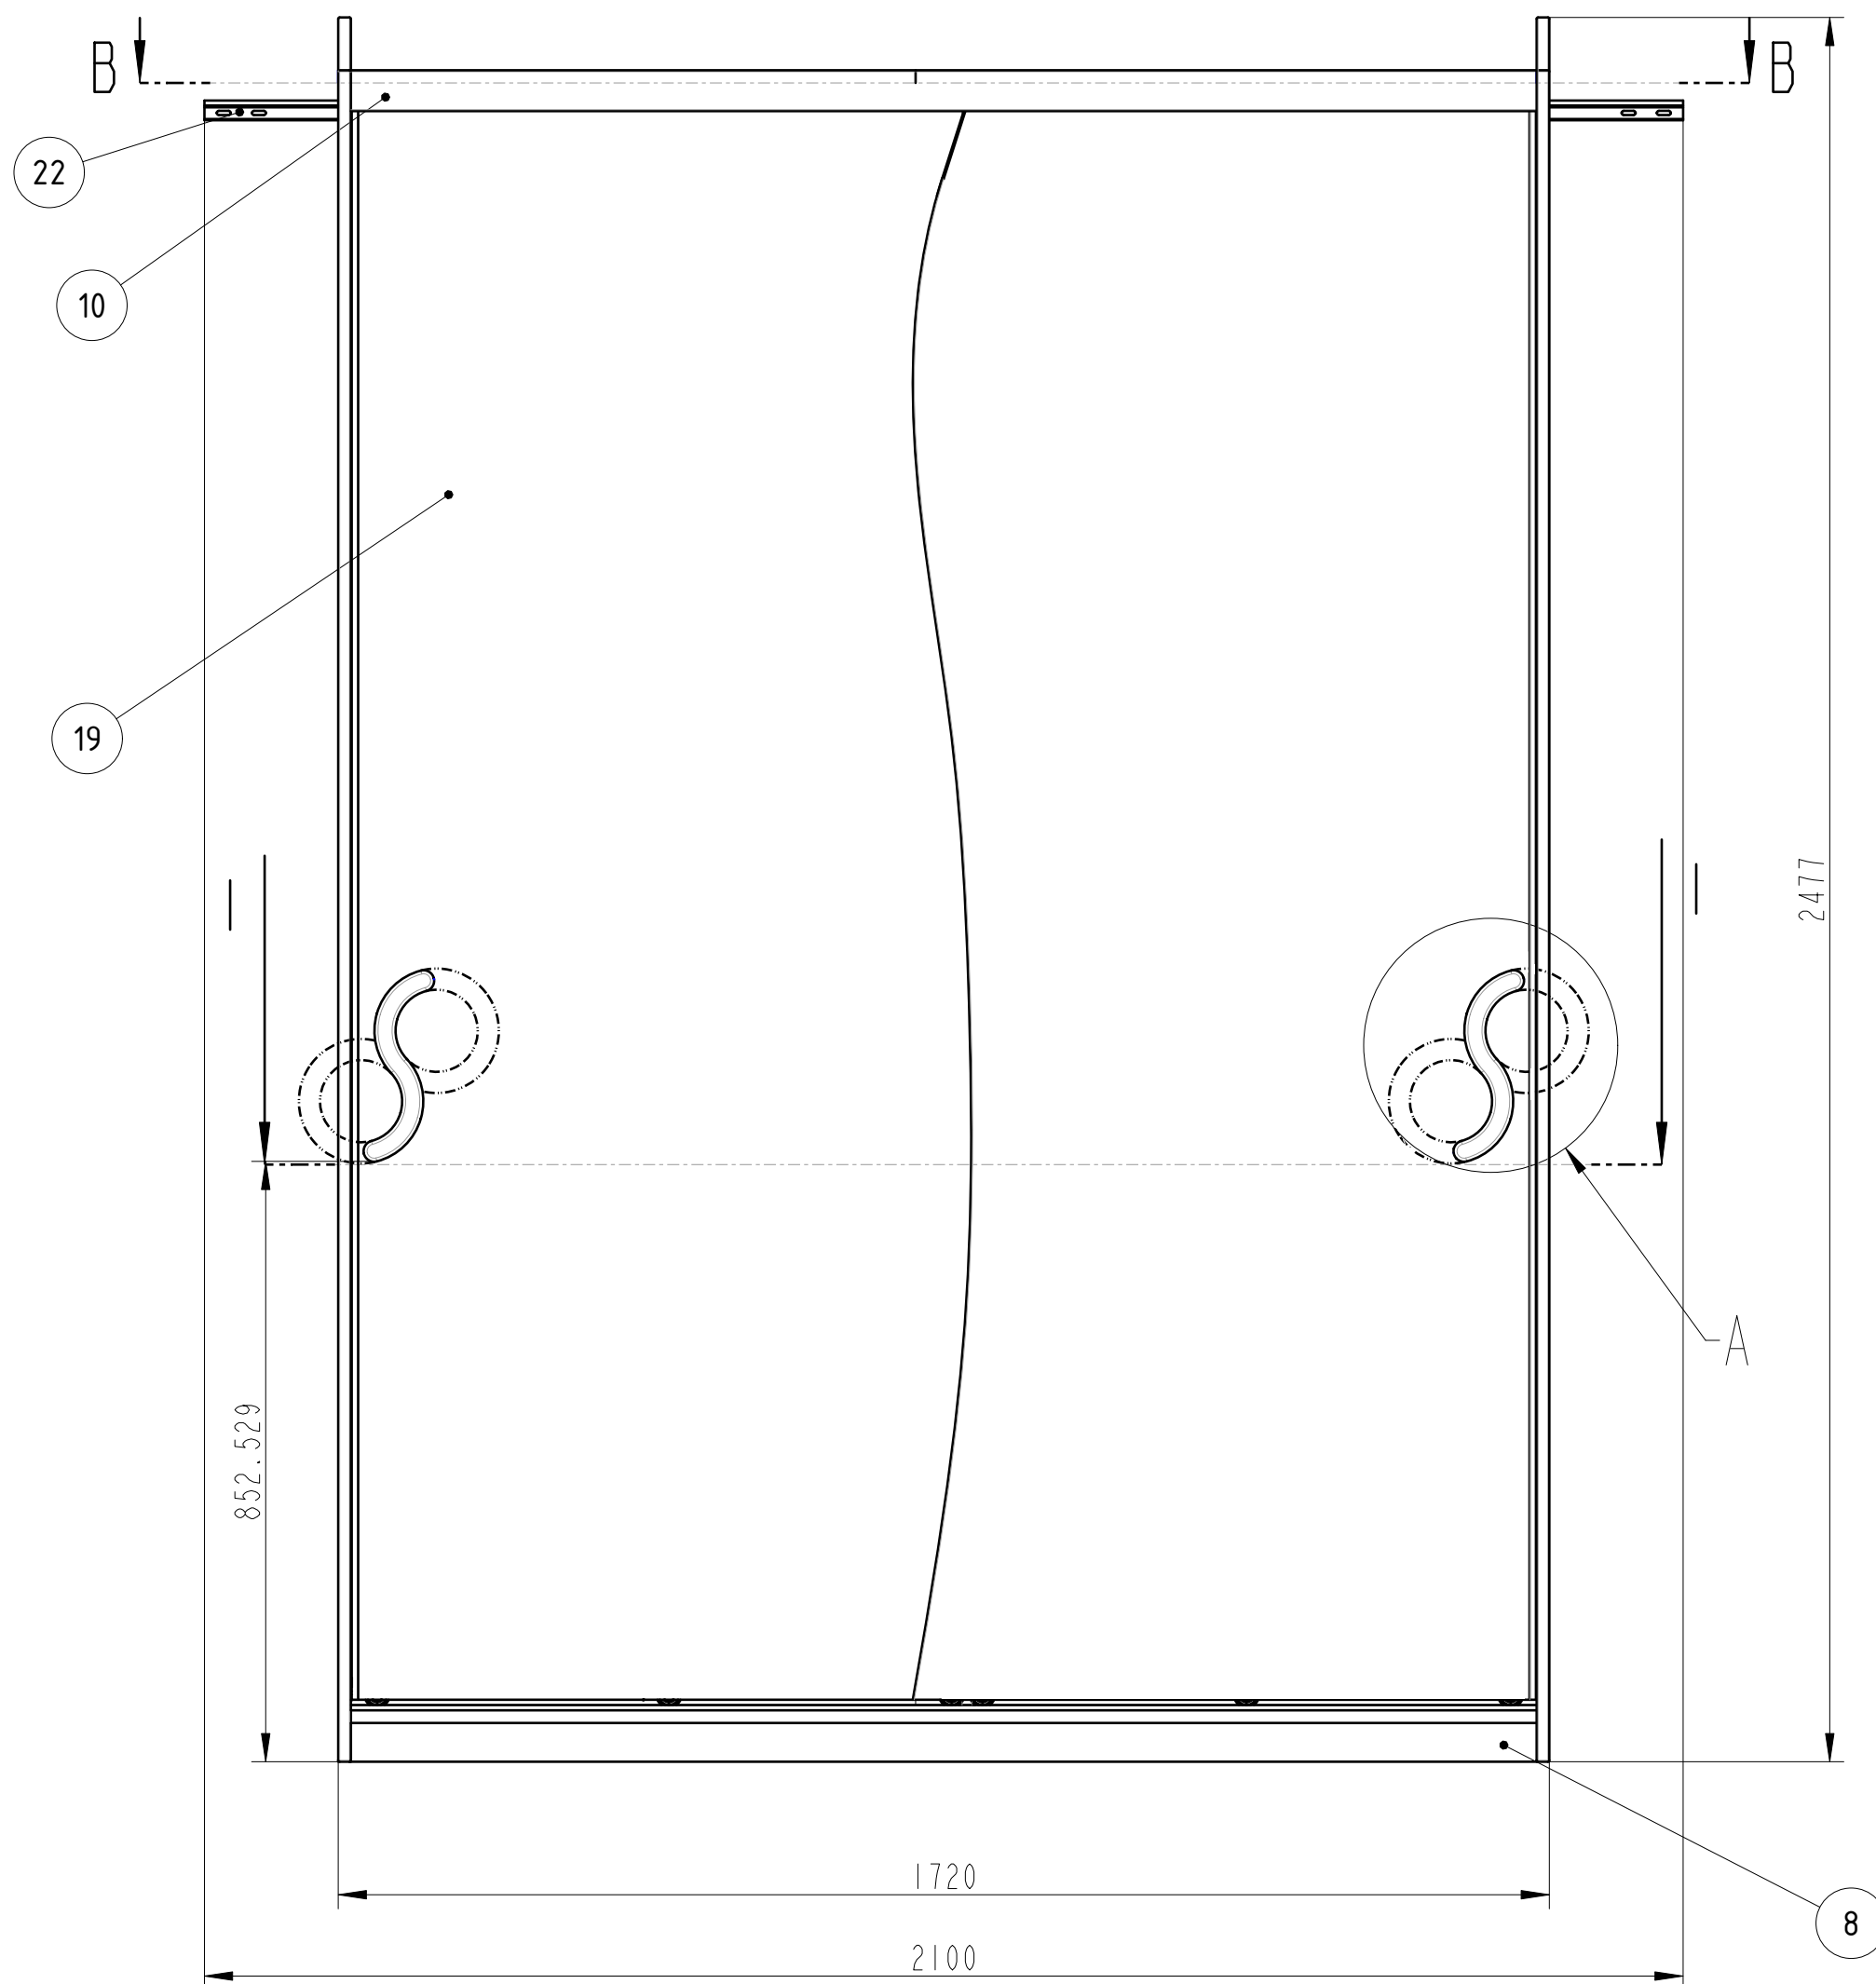


Méretezeten lekerekítések sugara: 2
A szekrény elemei vízszintes tengelyek mentén M5-ös súlyszettettfejú keresztornyos fűcsavarokkal és 7-es átmérőjű tiplikkel kerülnek rögzítésre.
A szekrény teteje és alja függőleges tengelyek mentén M5-ös excenteres bútorösszehúzó csavarokkal kerül rögzítésre.

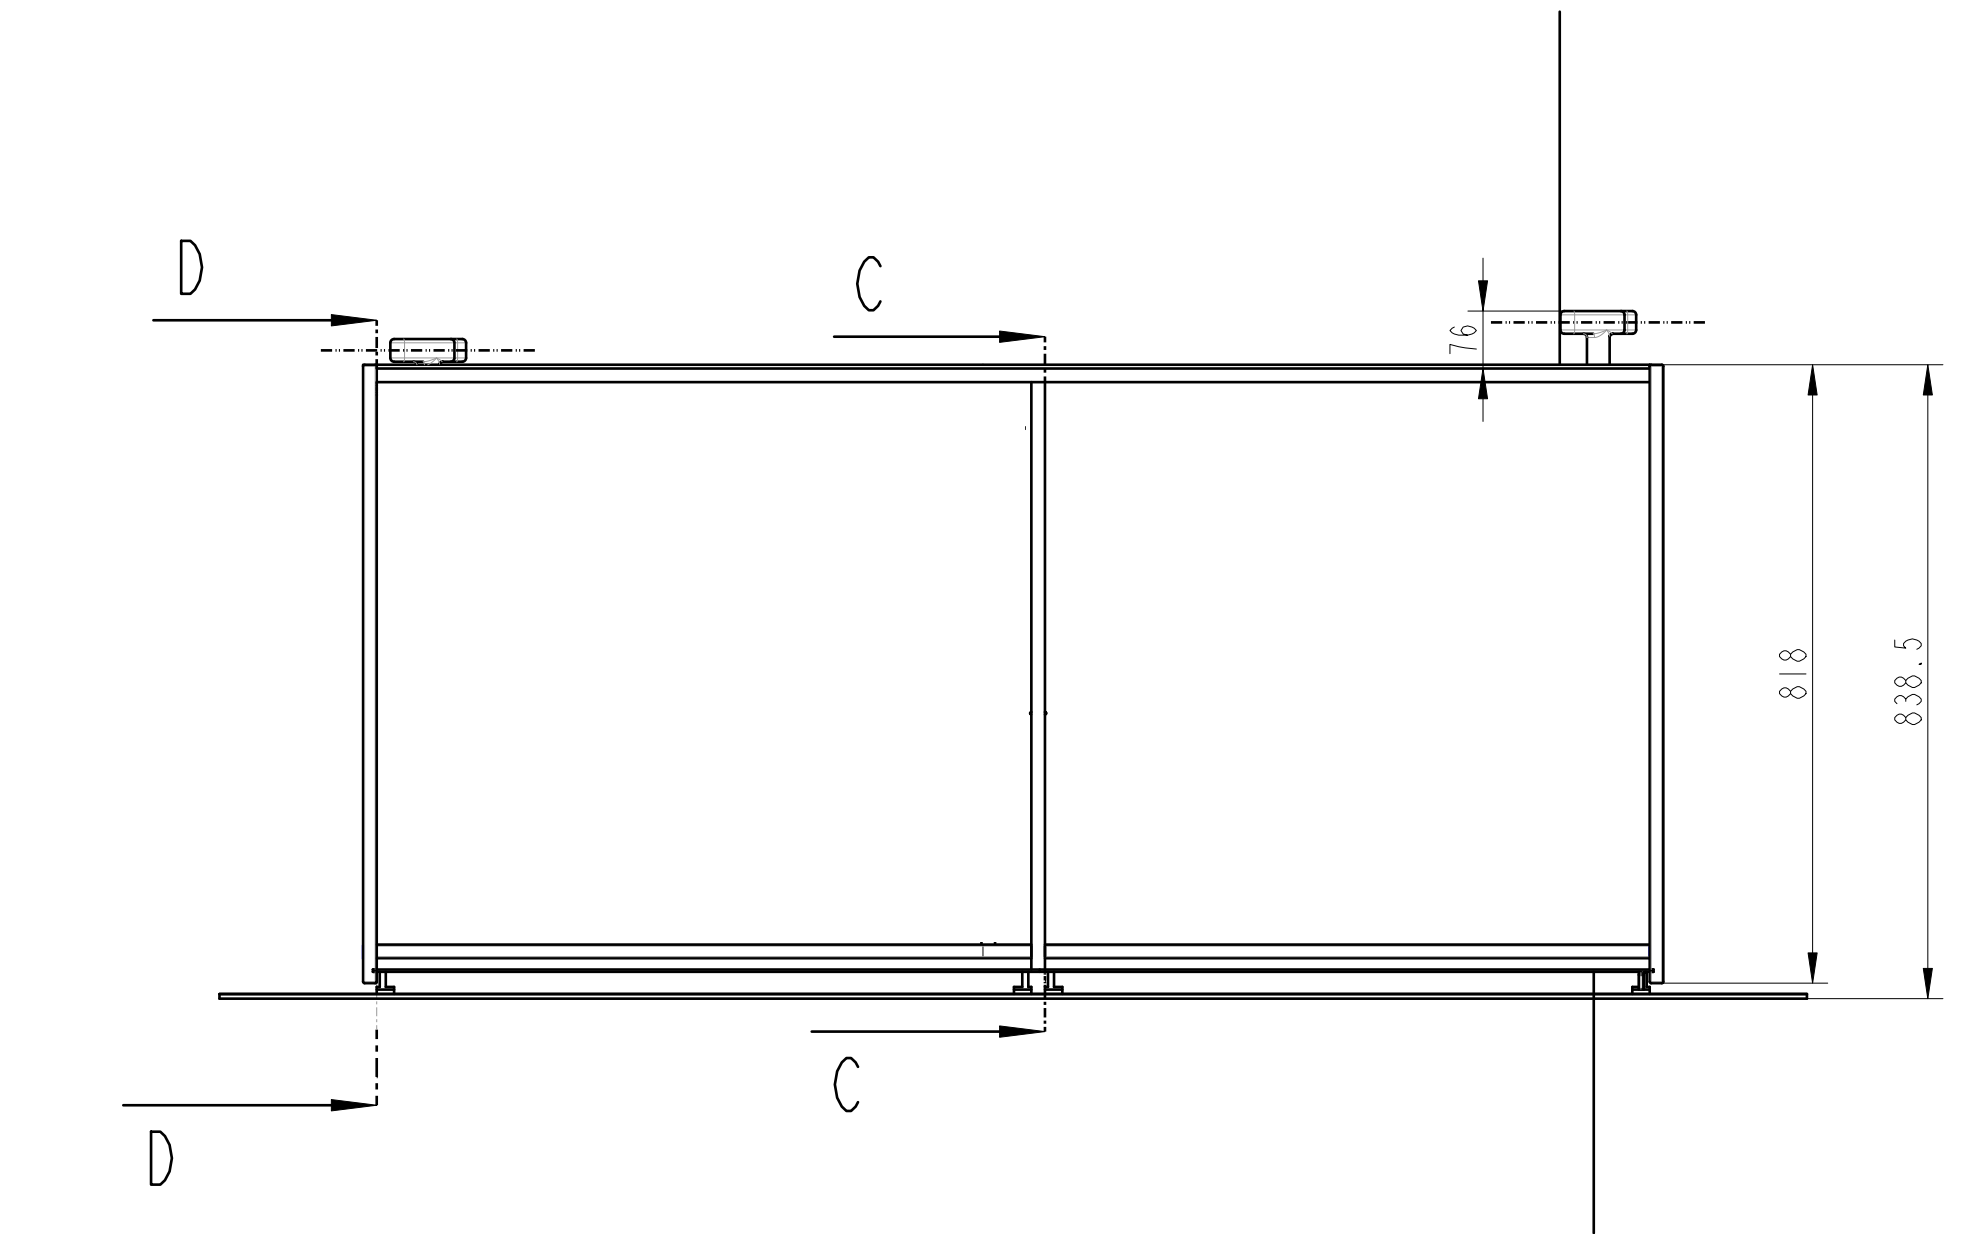

22	1	Hettich univerzális sín	2100x28x6,25	1007403	S235JR	0,099
21	4	Hettich faliszekrény-akasztó	101x40,7x27	9208645		0,032
20	1	RIEX VX47 ruhalift	808x800x137	HRF000594		17,066
19	1	Cosmo Gardrób tolóajtórendszer	1684x2311x166	BKSD-26-0400		40,930
18	1	Alacsony fiók	787x100x677	BKSD-26-0300		9,524
17	2	Fiók	787x200x677	BKSD-26-0200		10,204
16	1	Lehúzható polc	800x112x654	BKSD-26-0100		78,505
15	4	Vékony helykitöltő oldalsó panel	150x315x3	BKSD-26-0073 nyírfa		0,071
14	3	Helykitöltő oldalsó panel	150x315x18	BKSD-26-0072 nyírfa		0,425
13	1	Jobb hátsó összekötő elem	800x55x18	BKSD-26-0071 nyírfa		0,428
12	1	Bal hátsó összekötő elem	866x55x18	BKSD-26-0070 nyírfa		0,395
11	1	Rögzített rövid polc	866x340x18	BKSD-26-0054 nyírfa		2,650
10	1	Felső takaróelem	1684x58x18	BKSD-26-0039 nyírfa		0,876
9	2	Akasztorúdtartó	Ø60x18	BKSD-26-0035 nyírfa		0,022
8	1	Elülső összekötő elem	1684x55x18	BKSD-26-0033 nyírfa		0,834
7	1	Szekrény alja	1684x800x18	BKSD-26-0030 nyírfa		18,950
6	1	Rögzített akasztórúd	24x34x856	BKSD-26-0019 nyírfa		0,316
5	1	Elválasztófal	777x2384x18	BKSD-26-0014 nyírfa		14,622
4	1	Rögzített polc	800x680x18	BKSD-26-0013 nyírfa		4,910
3	2	Szekrény hátulja	812x2402x3	BKSD-26-0012 nyírfa		2,921
2	1	Szekrény teteje	1684x782x18	BKSD-26-0011 nyírfa		11,852
1	2	Szekrény oldala	814x2473x18	BKSD-26-0010 nyírfa		17,910

Tsz	Db	Megnevezés	Méret	Rajzszám	Rajzszám	Tömeg
				Cikkszám		(kg)
Tervező:		Gyártmány:	Méretarány:			
Irázi-Tihor Noémi		Ruhásszekrény	1:10			BME GÉP- ÉS TERMÉKTERVEZÉS TANSZÉK
Dátum:		Megnevezés:		Vet. mód:	Rajzszám:	
2026. 06. 04.		Törzsrajz				
Ellenőrizte:		Anyag:	Tömeg:			
Varga András						BKSD-26-1000